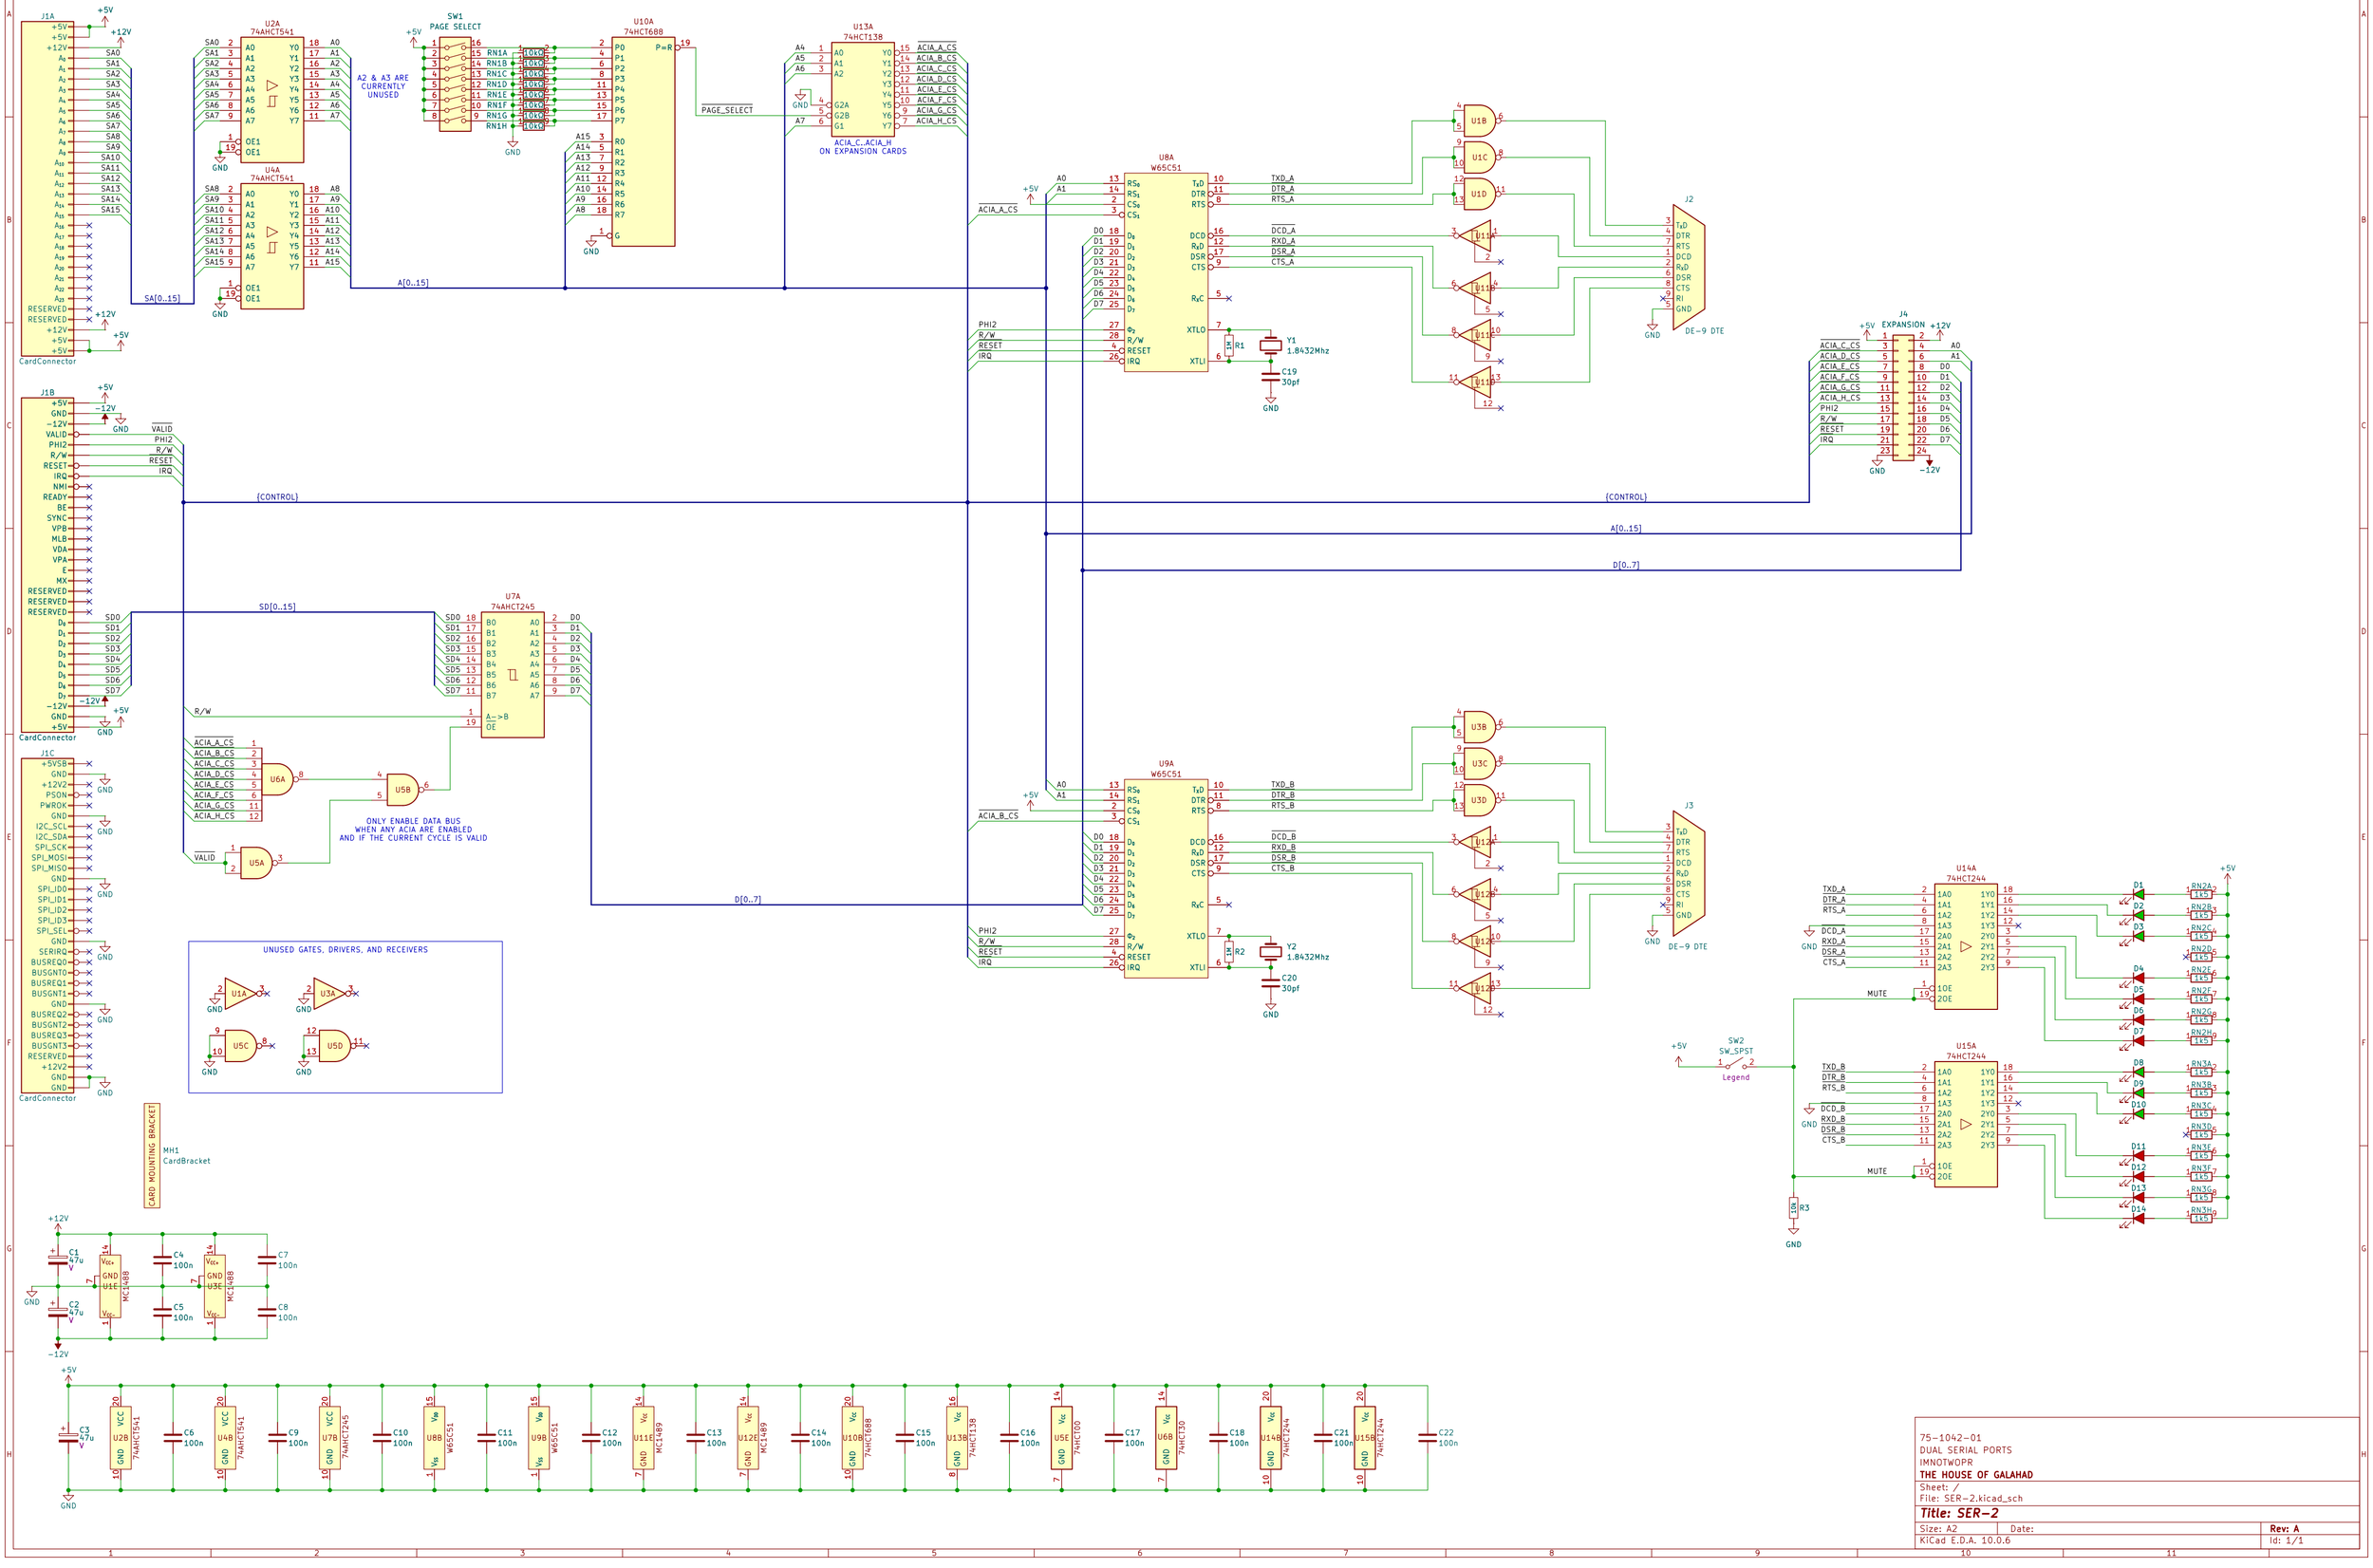


75-1042-01	
DUAL SERIAL PORTS	
IMNOTWOPR	
THE HOUSE OF GALAHAD	
Sheet: /	
File: SER-2.kicad_sch	
Title: SER-2	
Size: A2	Date:
KiCad E.D.A. 10.0.6	**Rev: A**
	Id: 1/1