


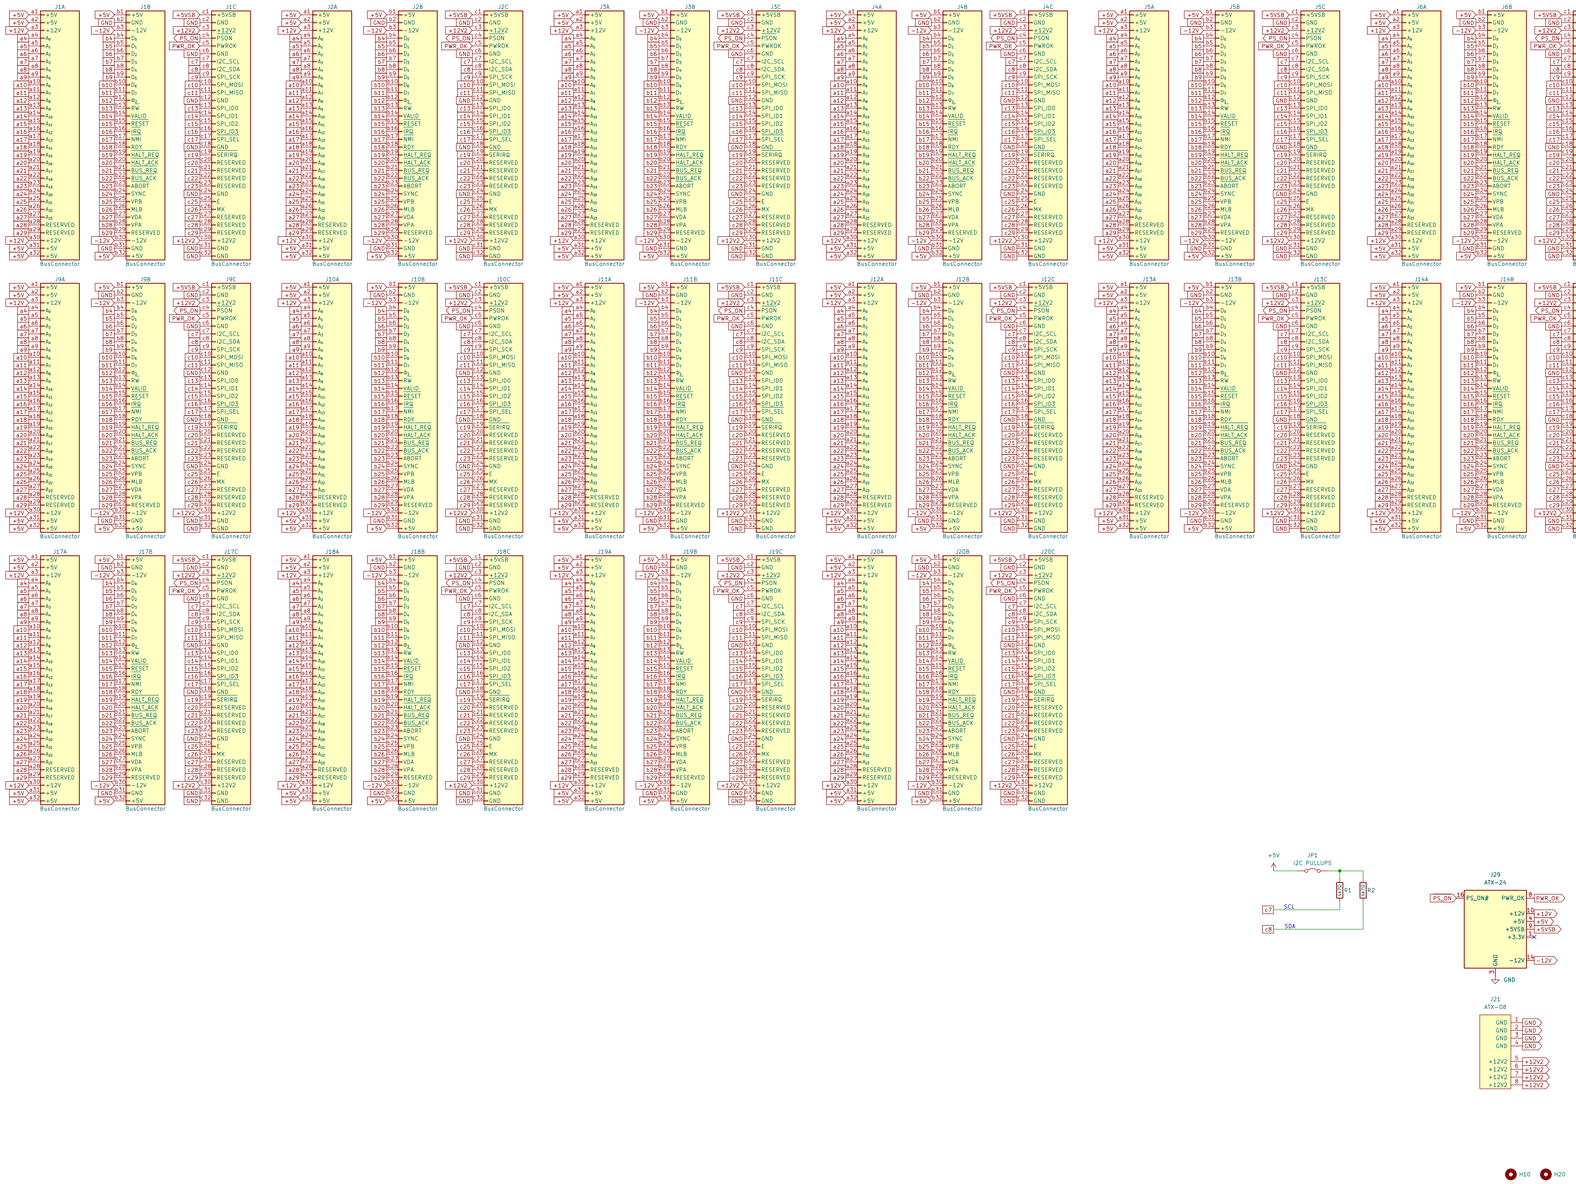

IMNOTWOPR
THE HOUSE OF GALAHAD

Sheet: /
File: BACKPLANE.kicad_sch

Title: BACKPLANE

Size: A1	Date:	**Rev: A**
KiCad E.D.A. 10.0.6		Id: 1/1